


图1 · 一带总览：一线三折两翼七节点

- 临时粗略边界(provisional)
- 京张 Hyper Line 主脊

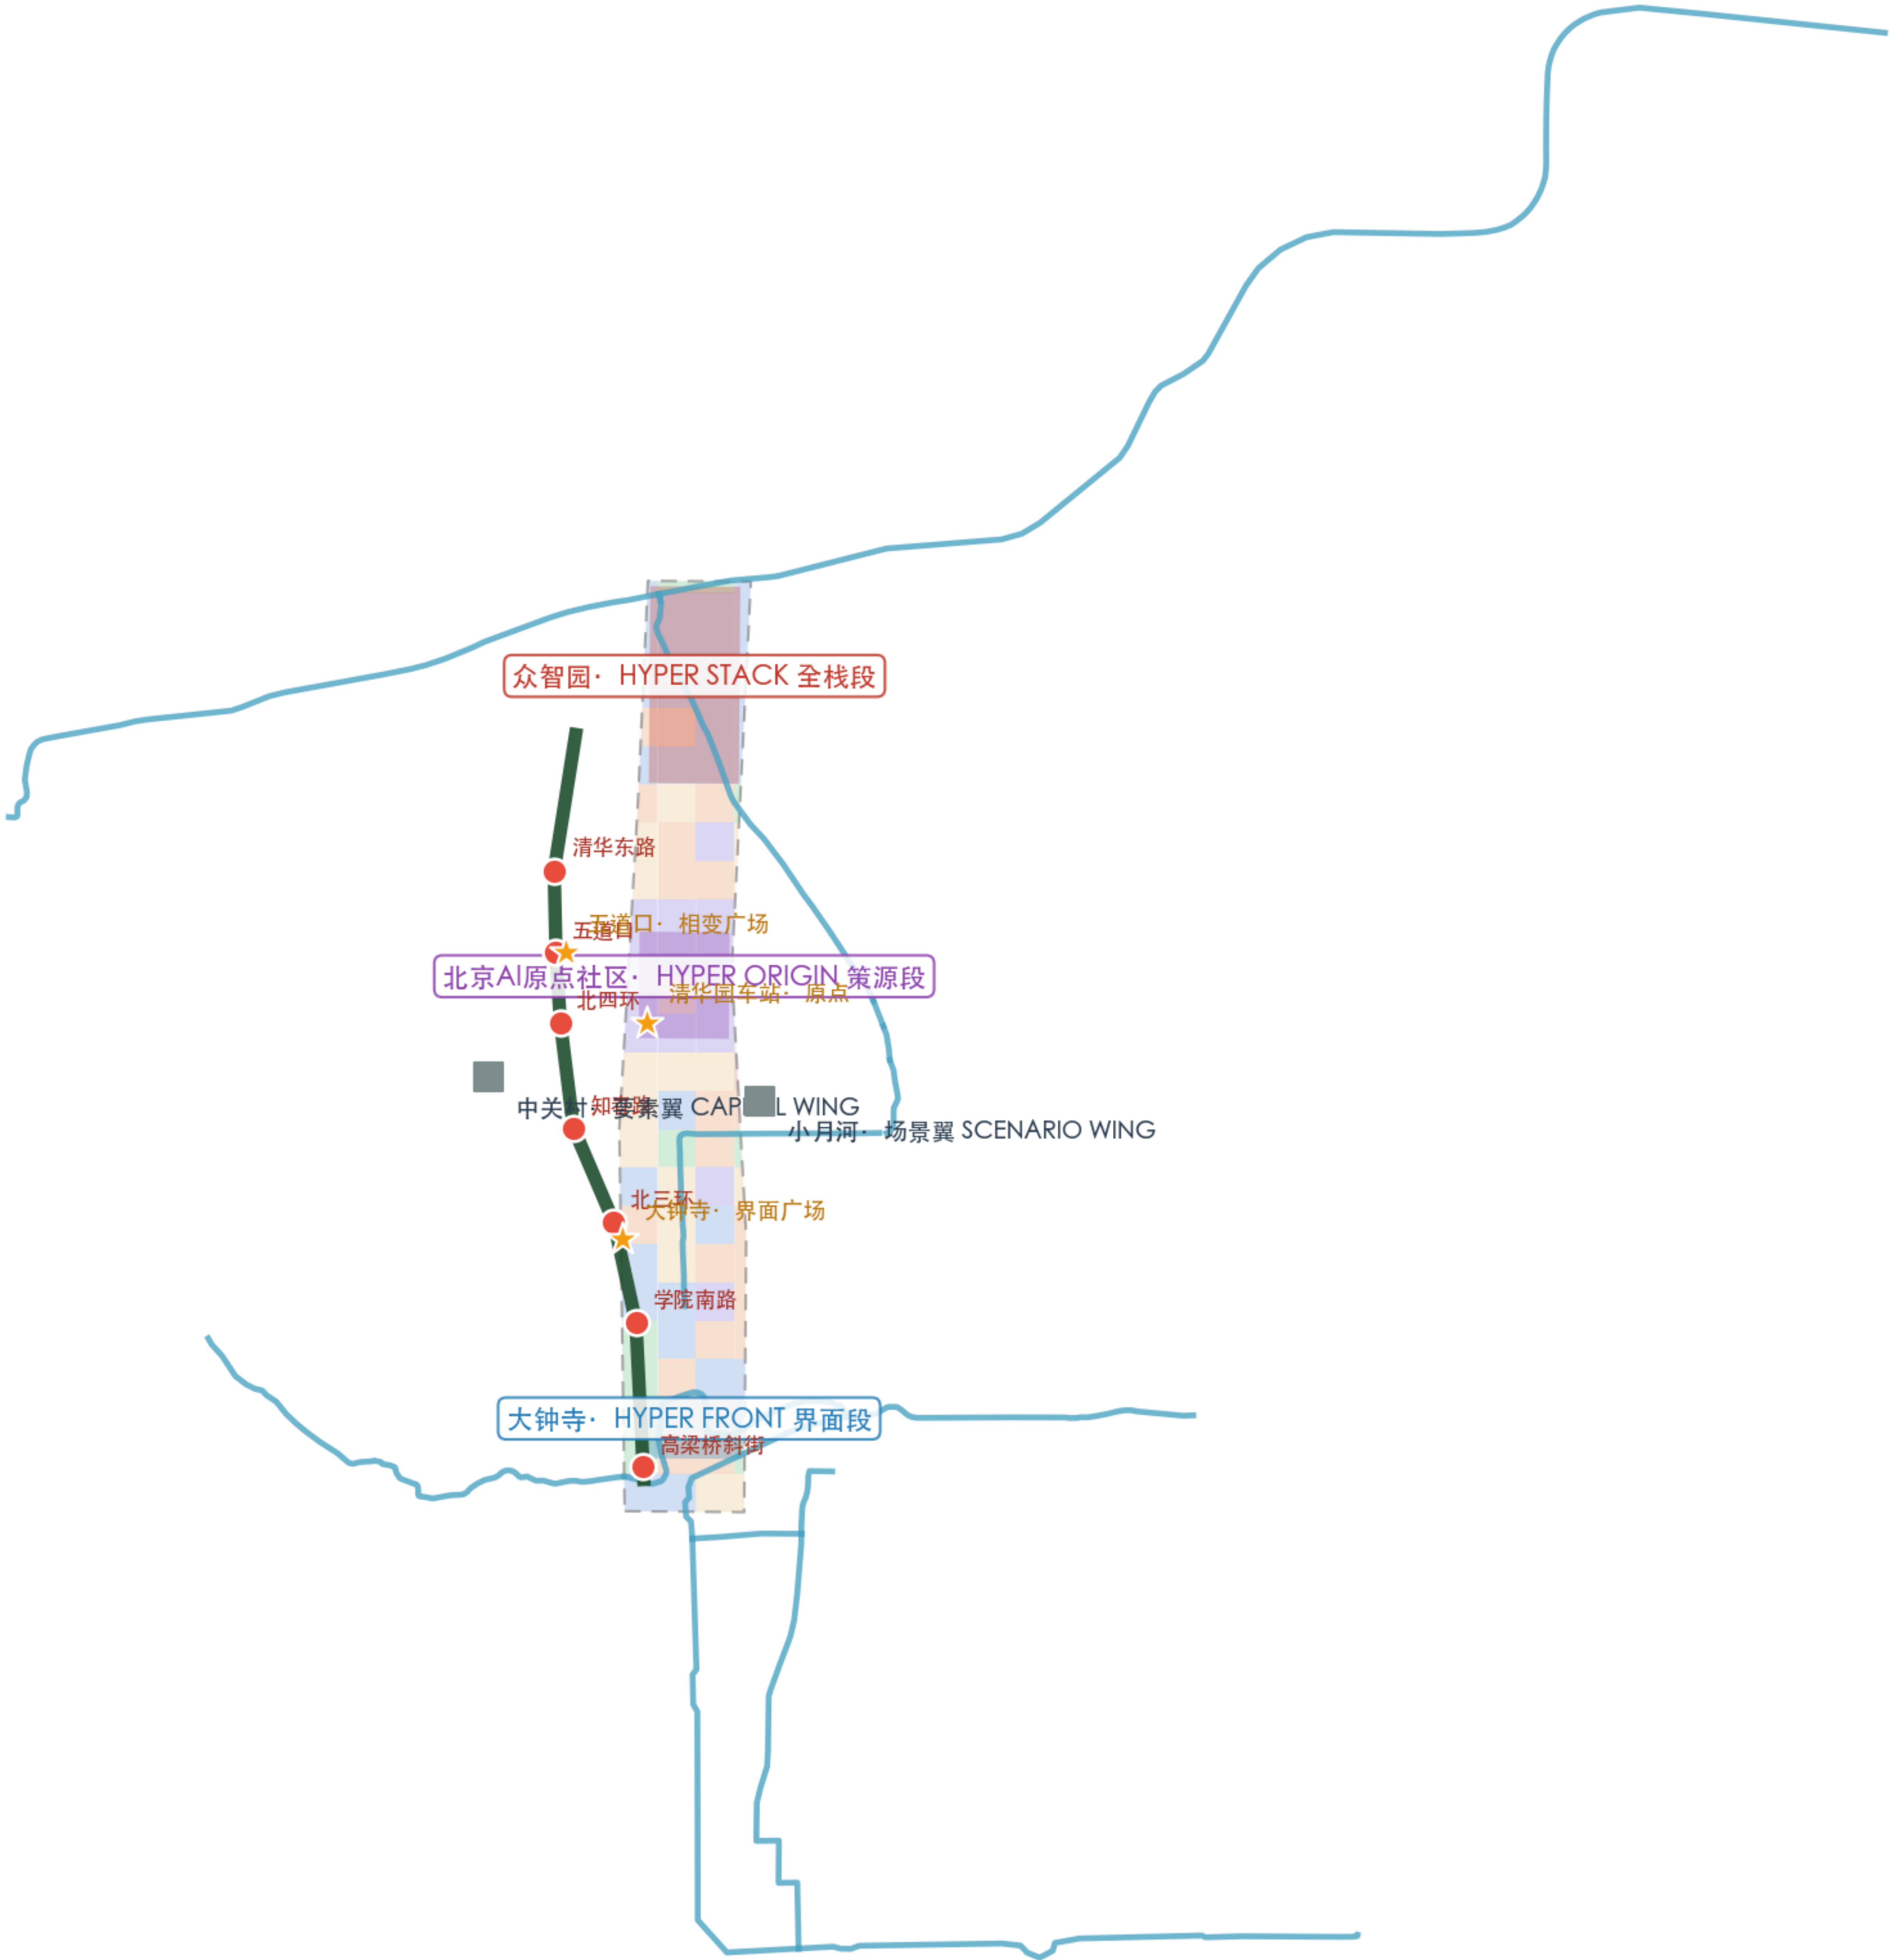

来源：官方公告+OSM现状+高德POI（2026-08-15）；临时边界仅虚线表达，非官方红线；全部为概念建议

图2 · 三层范围传导与用地结构 (provisional 边界为虚线约束，重点在分区逻辑与职住判断)

图2a · 用地结构与 POI 动力分区 (概念)

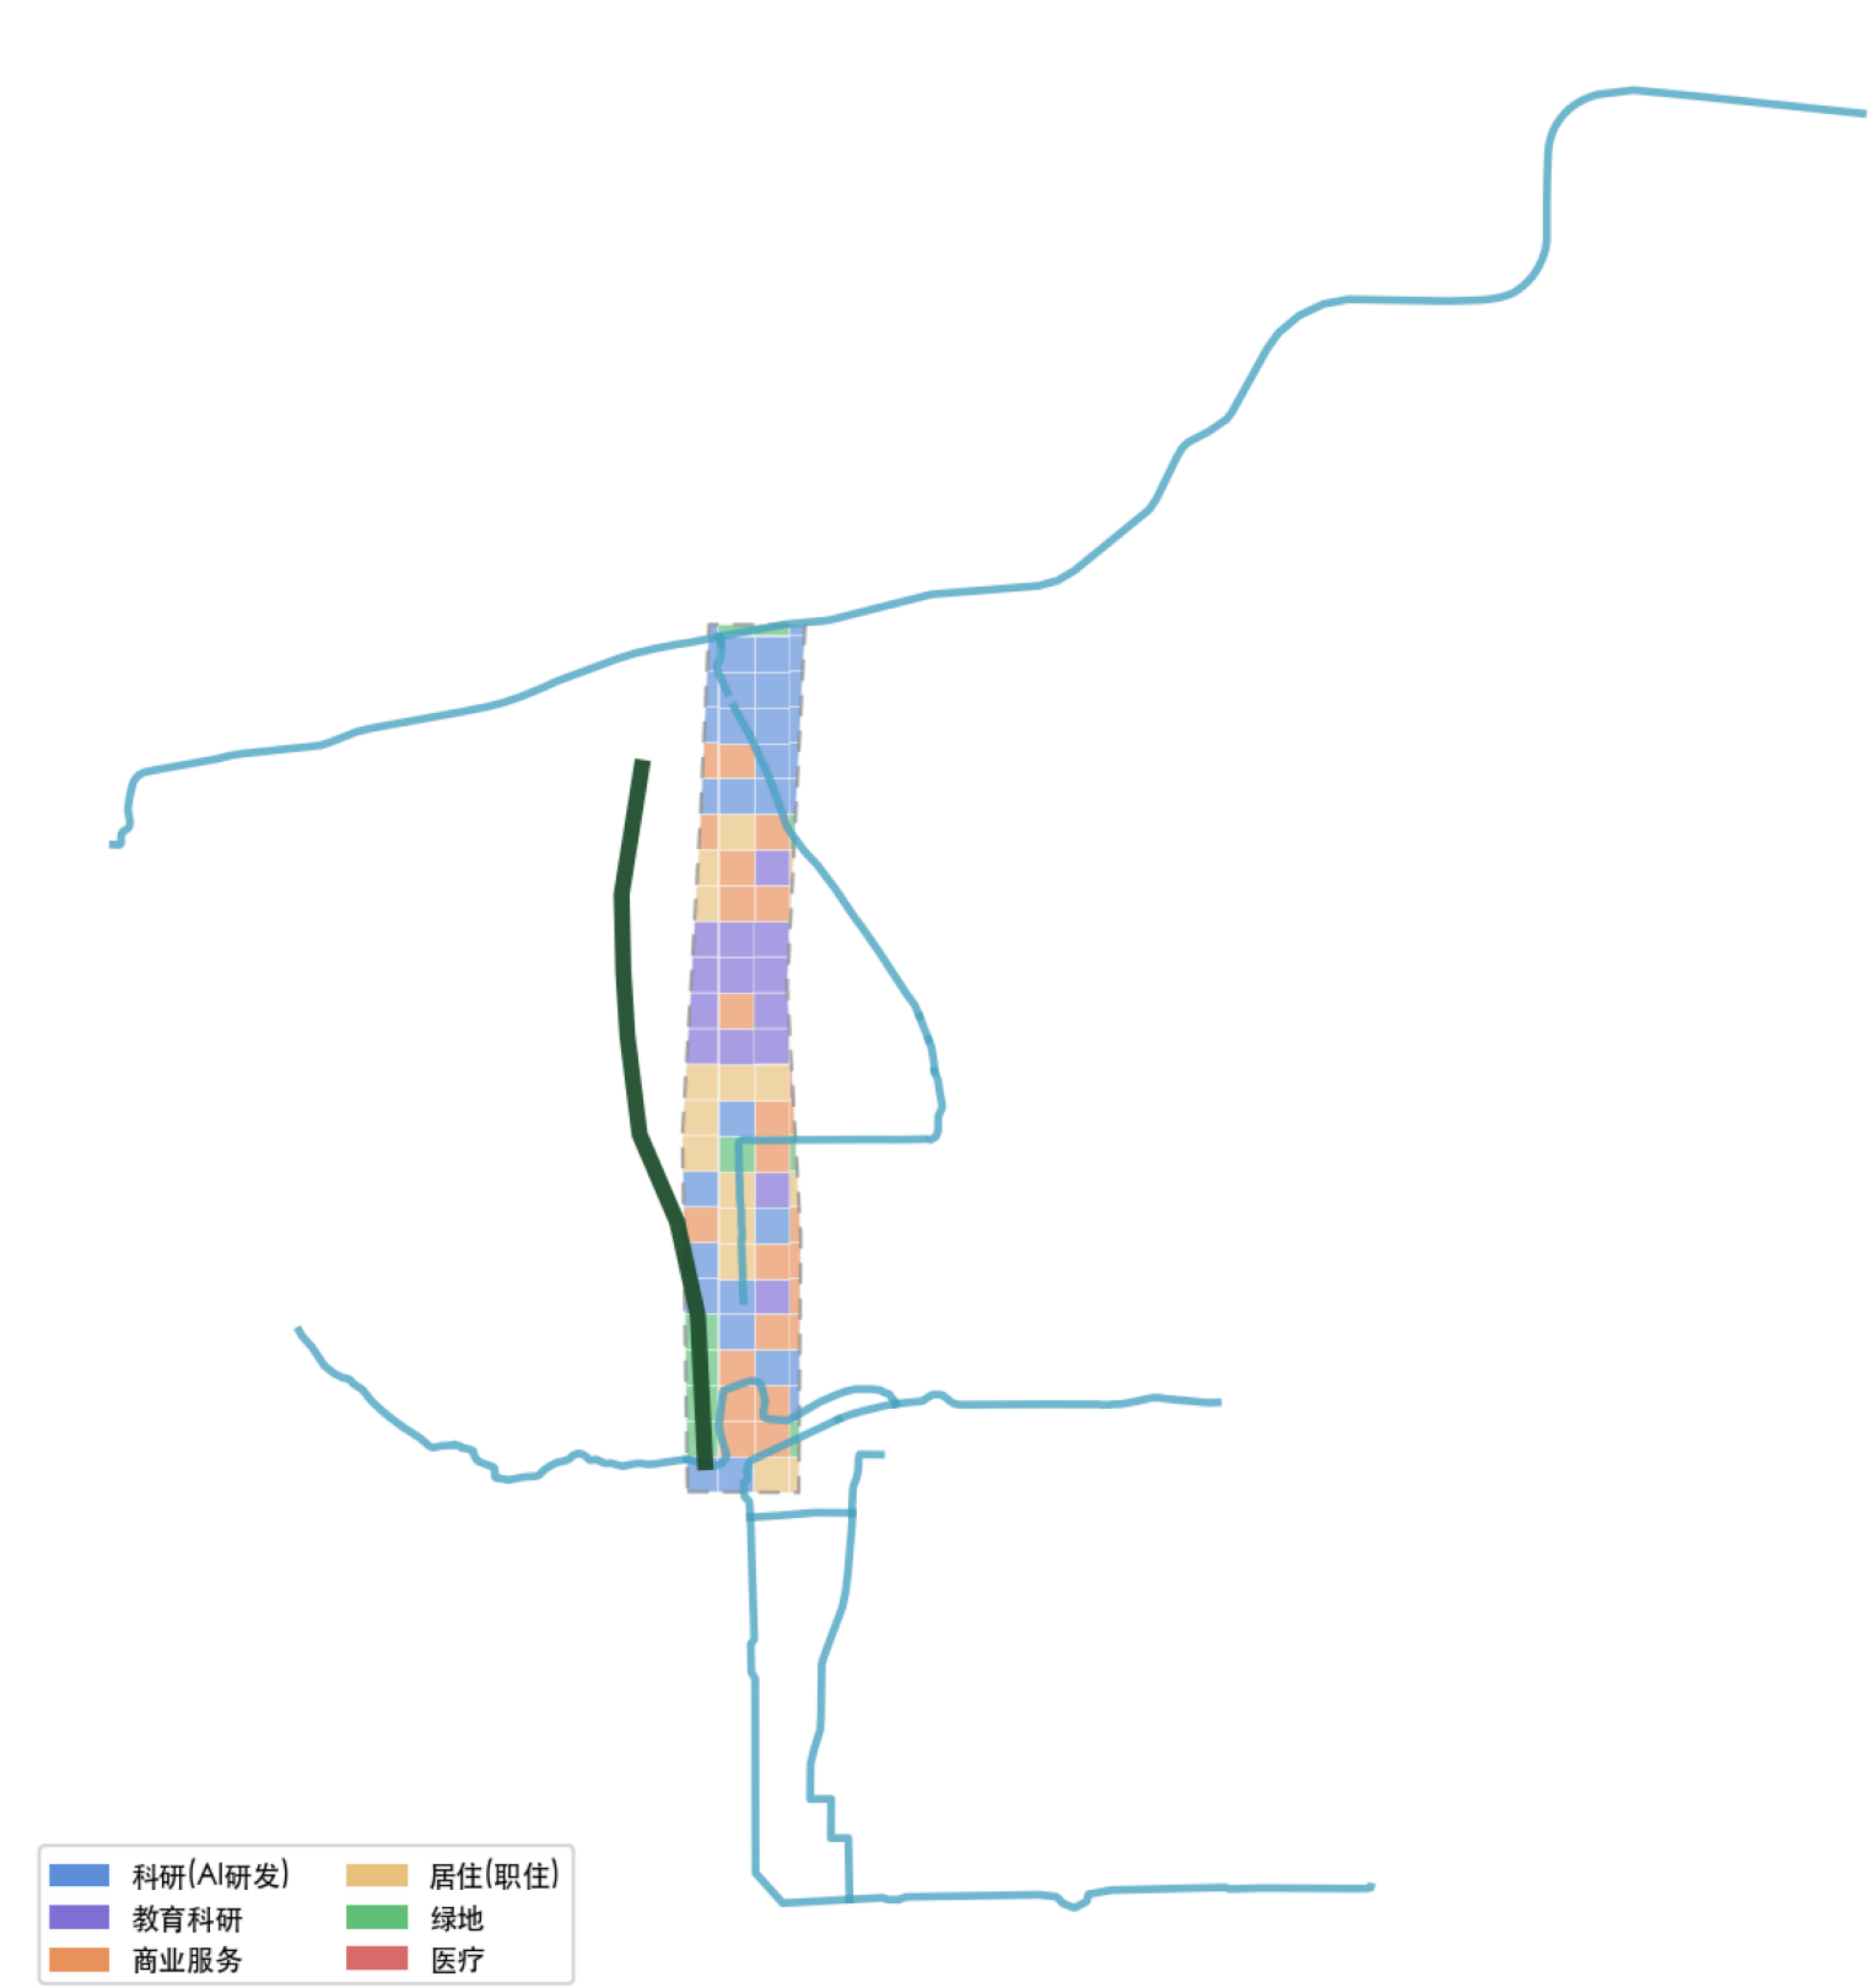


图2b · 用地构成 (万 m²，概念分区)





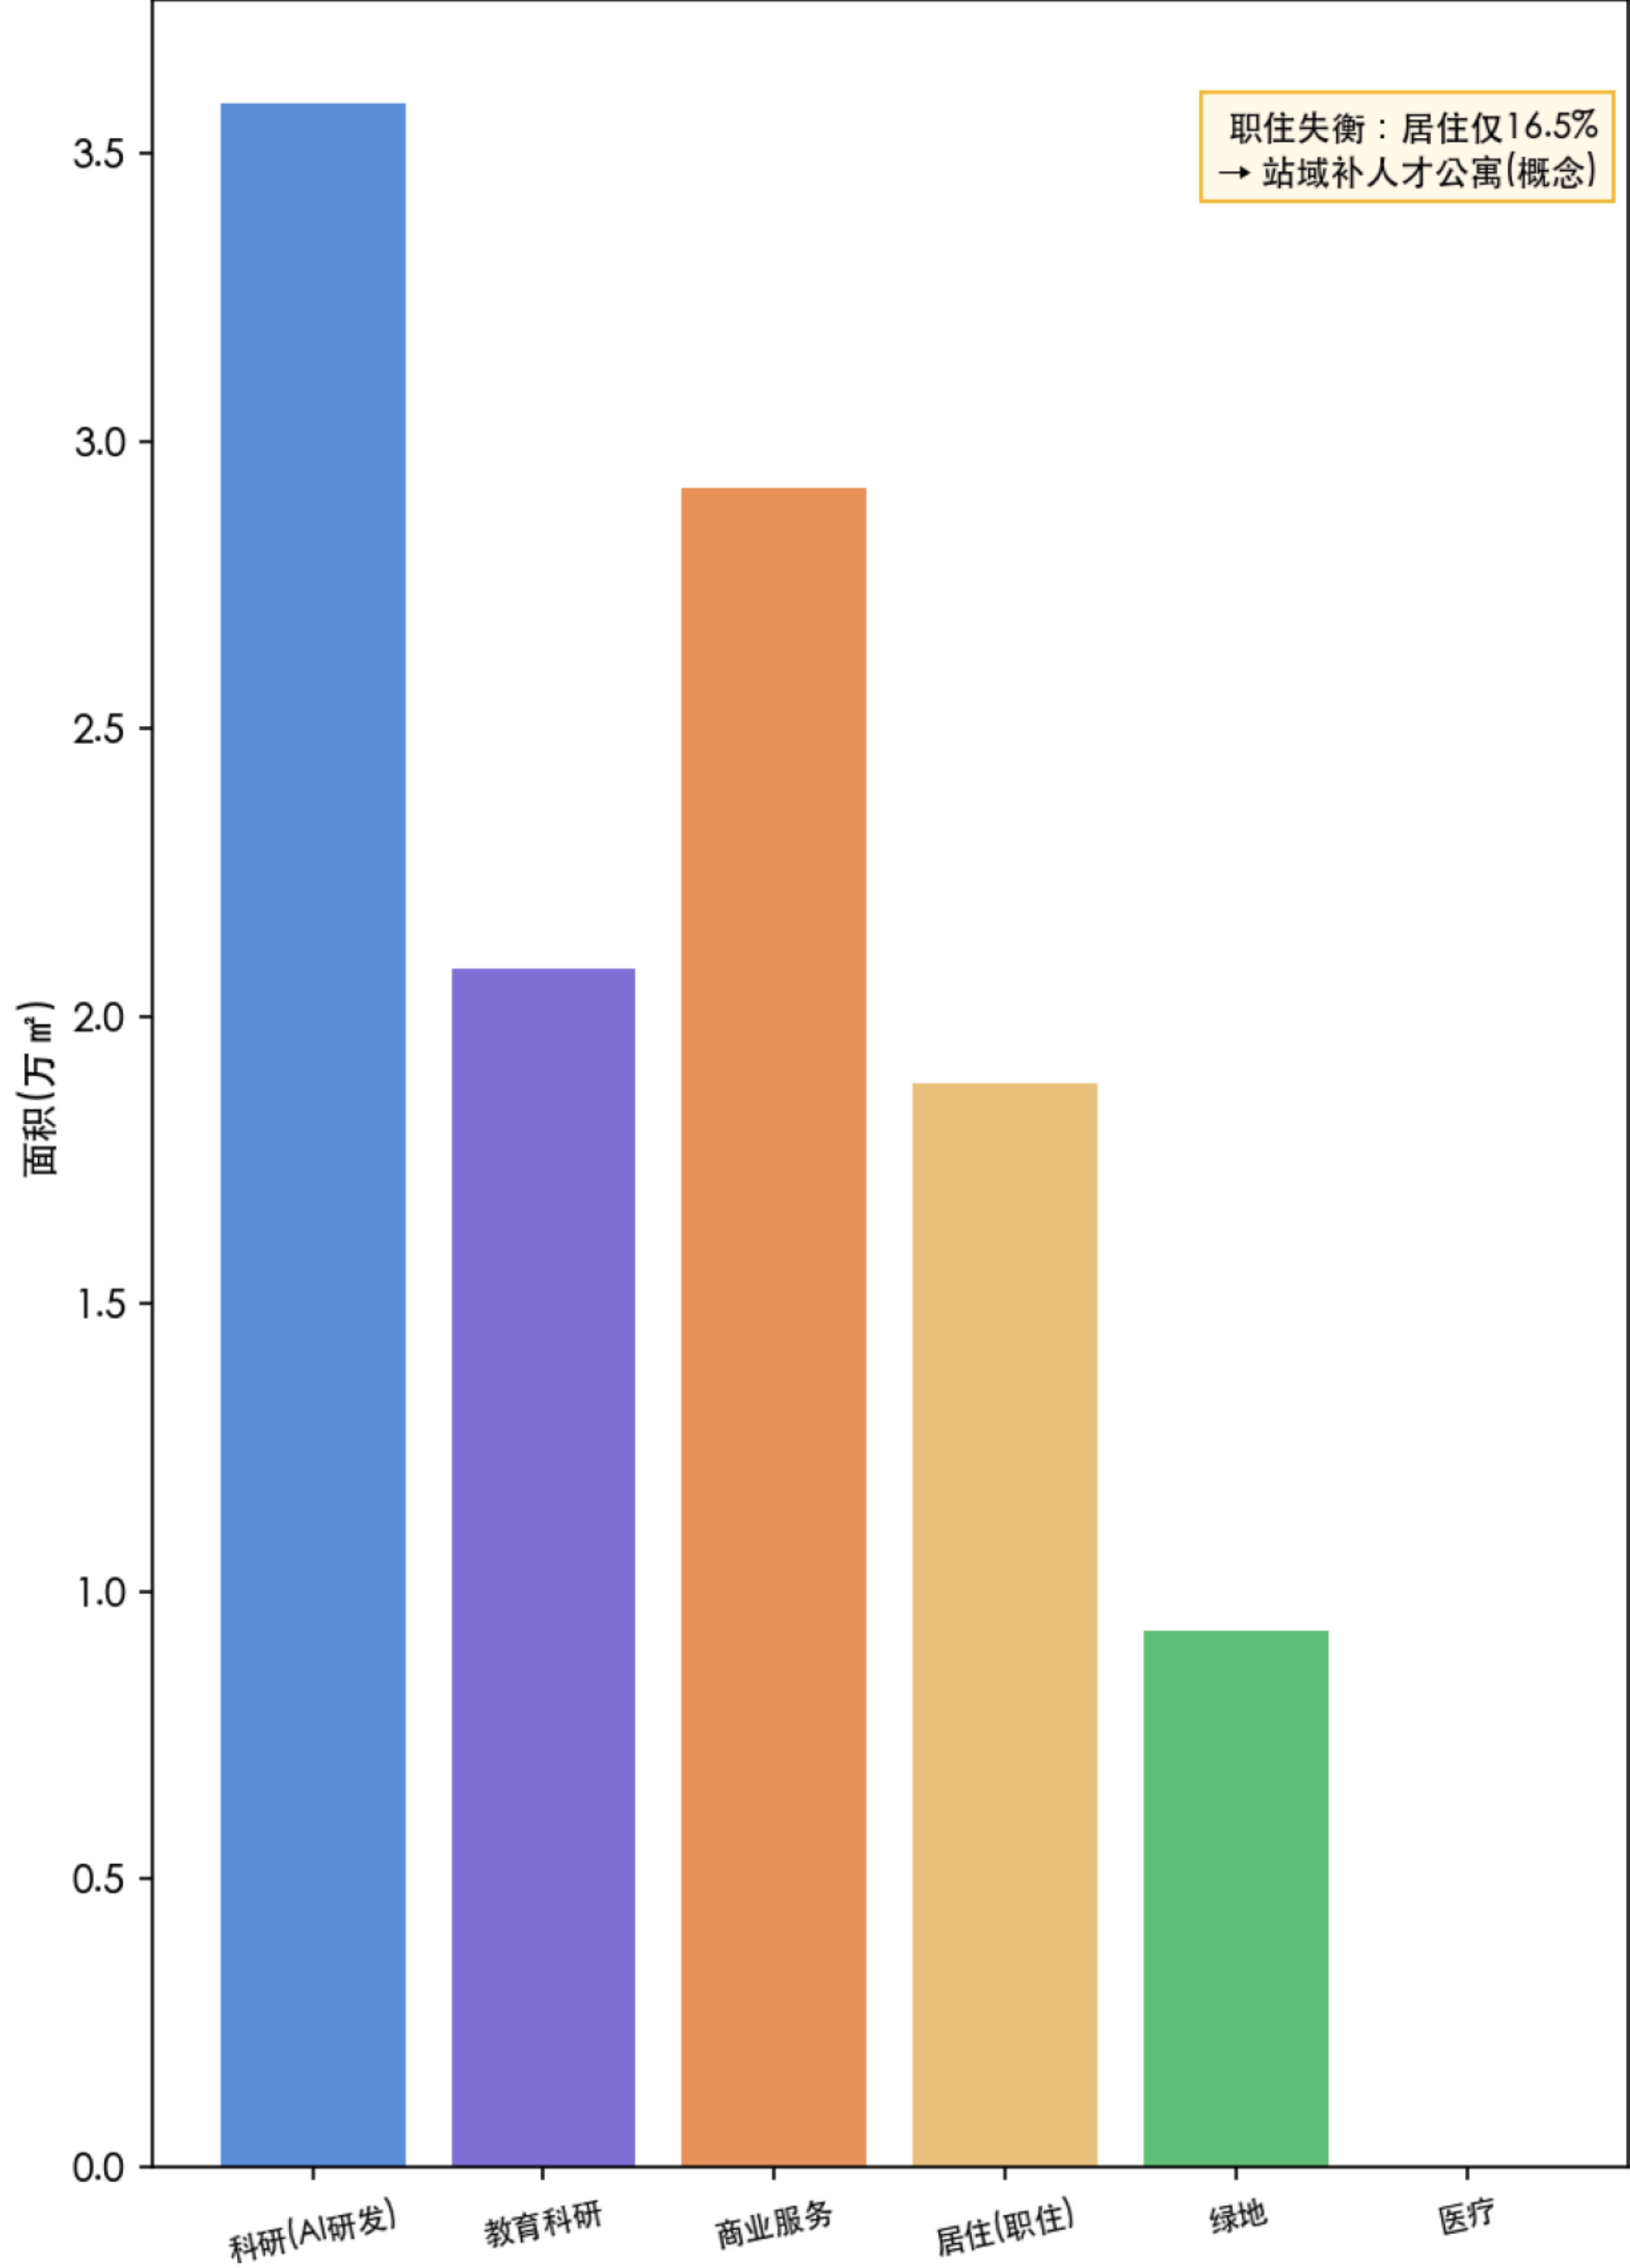


图4 · 交通慢行与蓝绿系统：七节点缝合

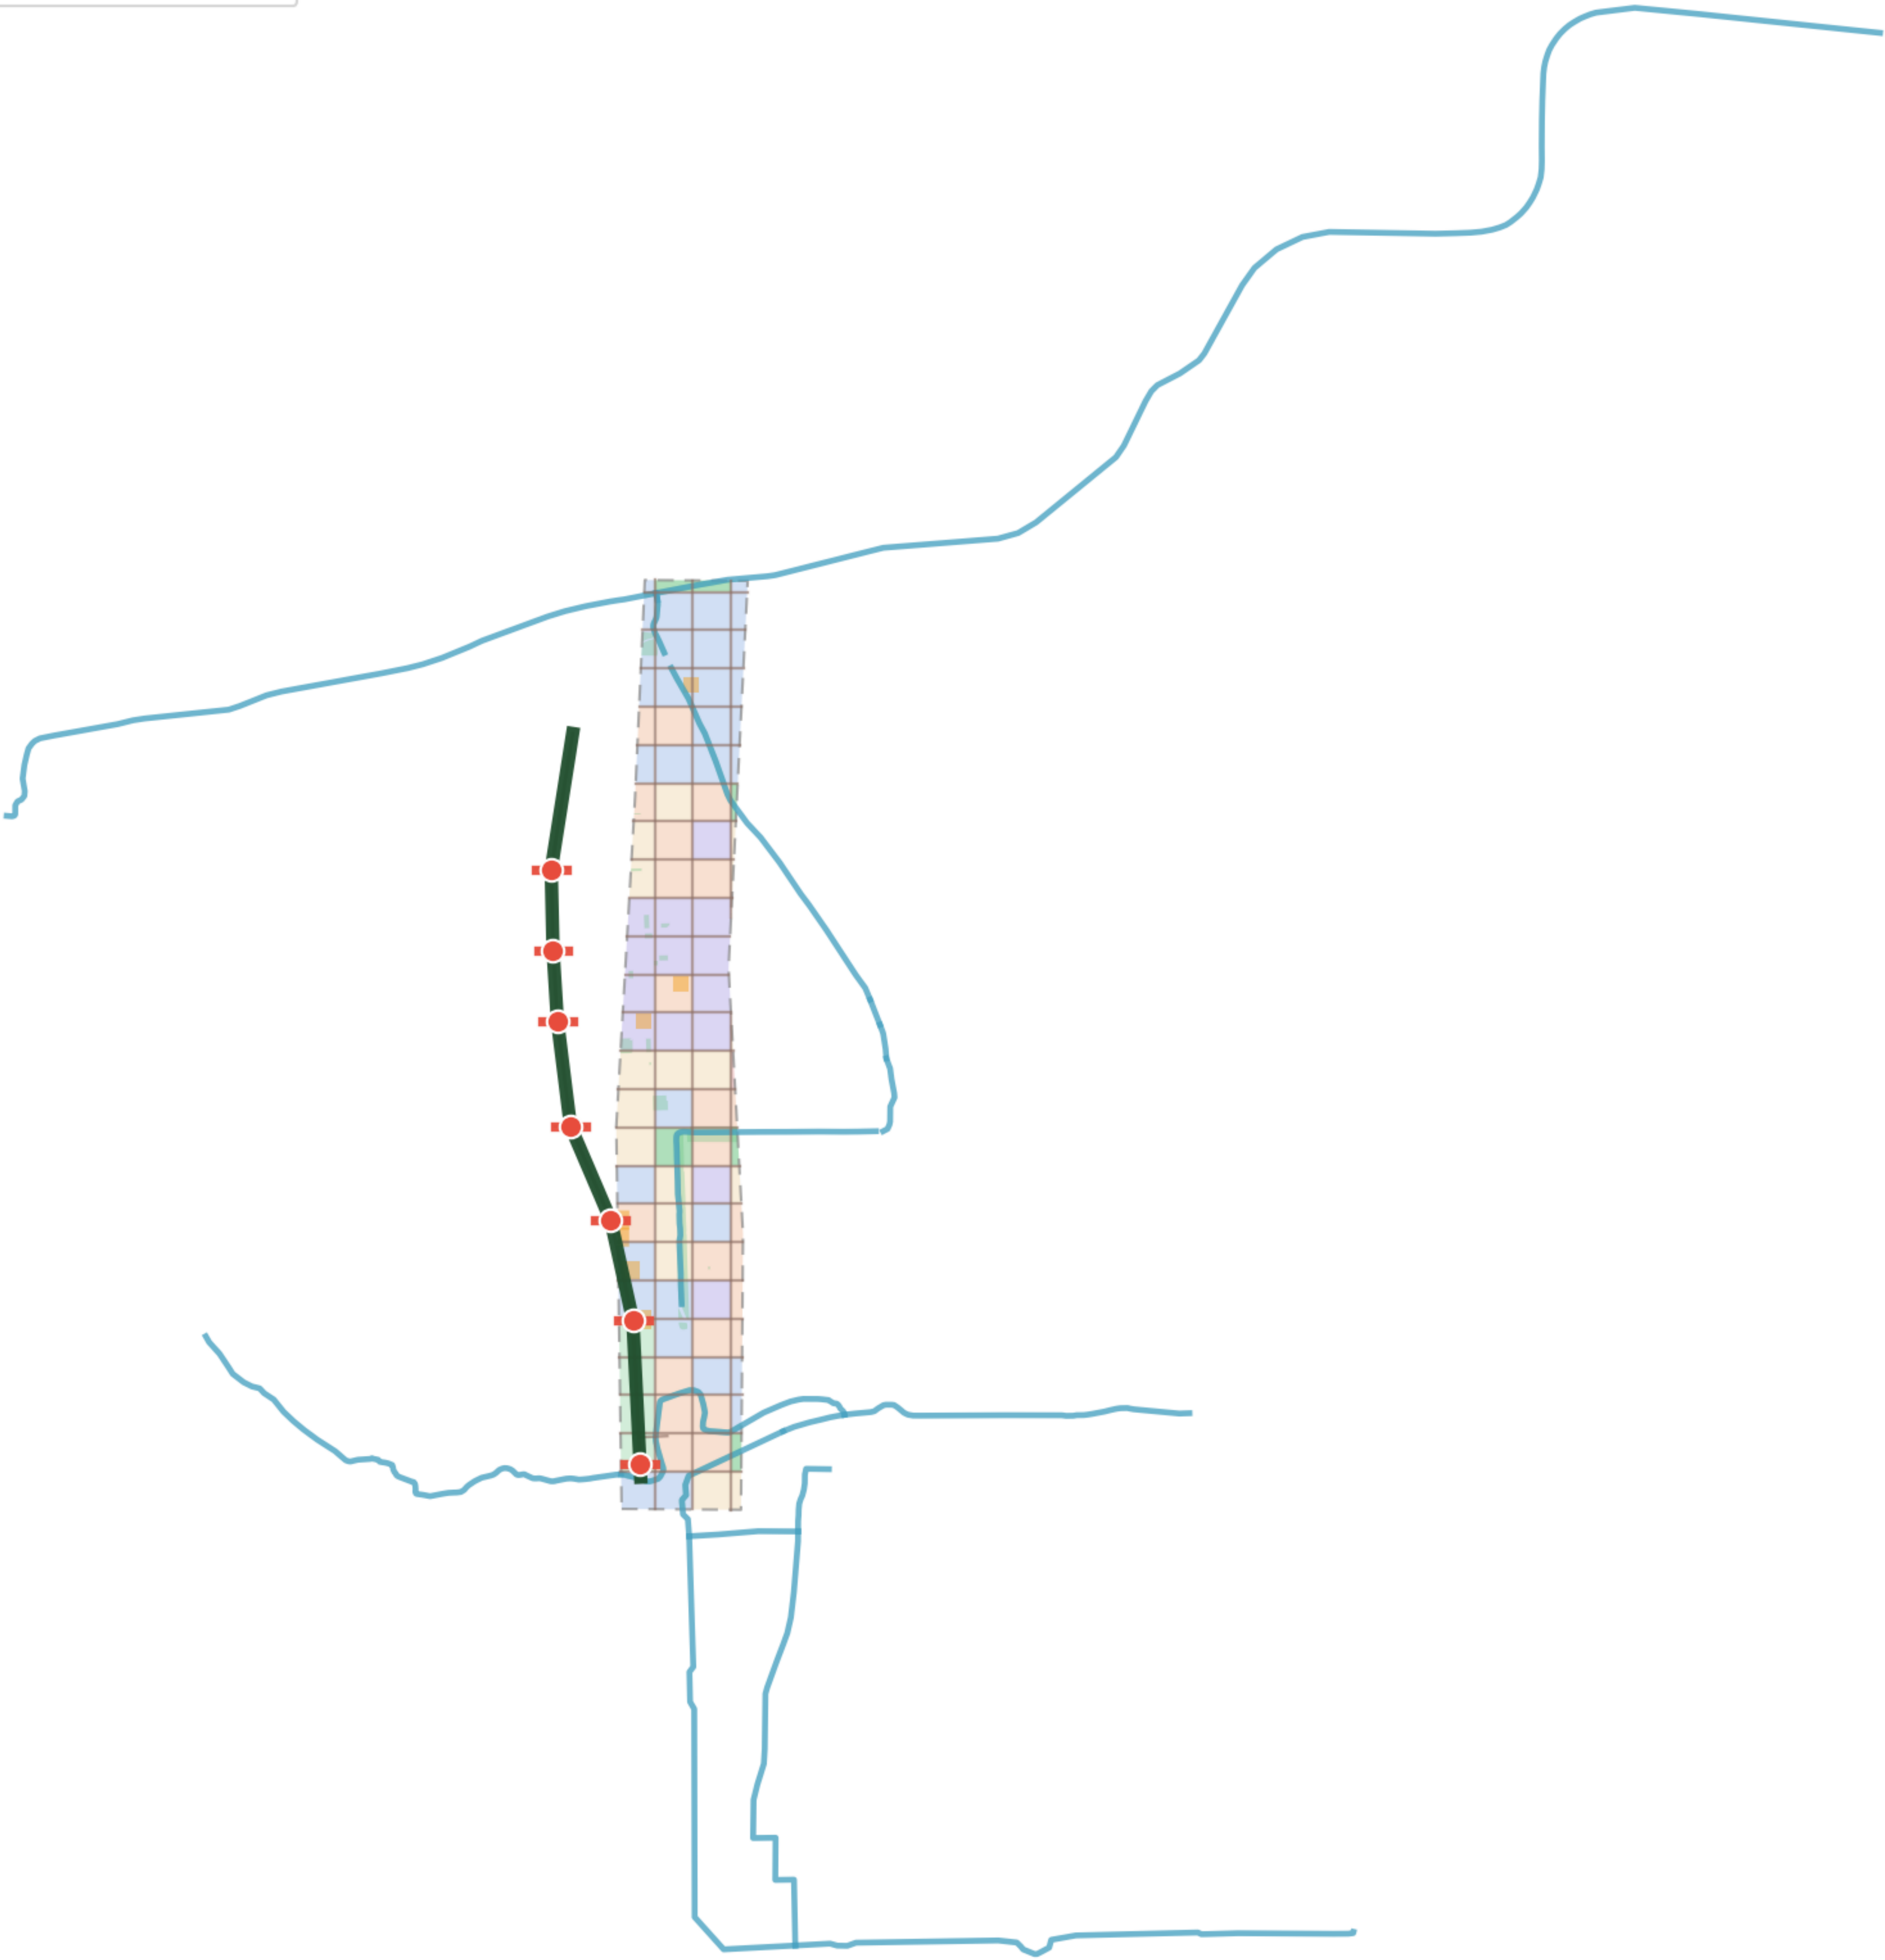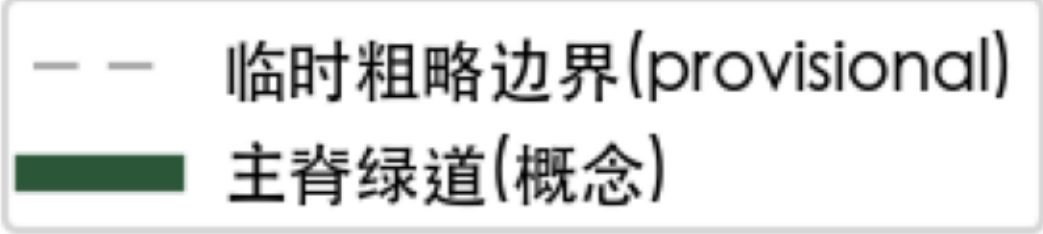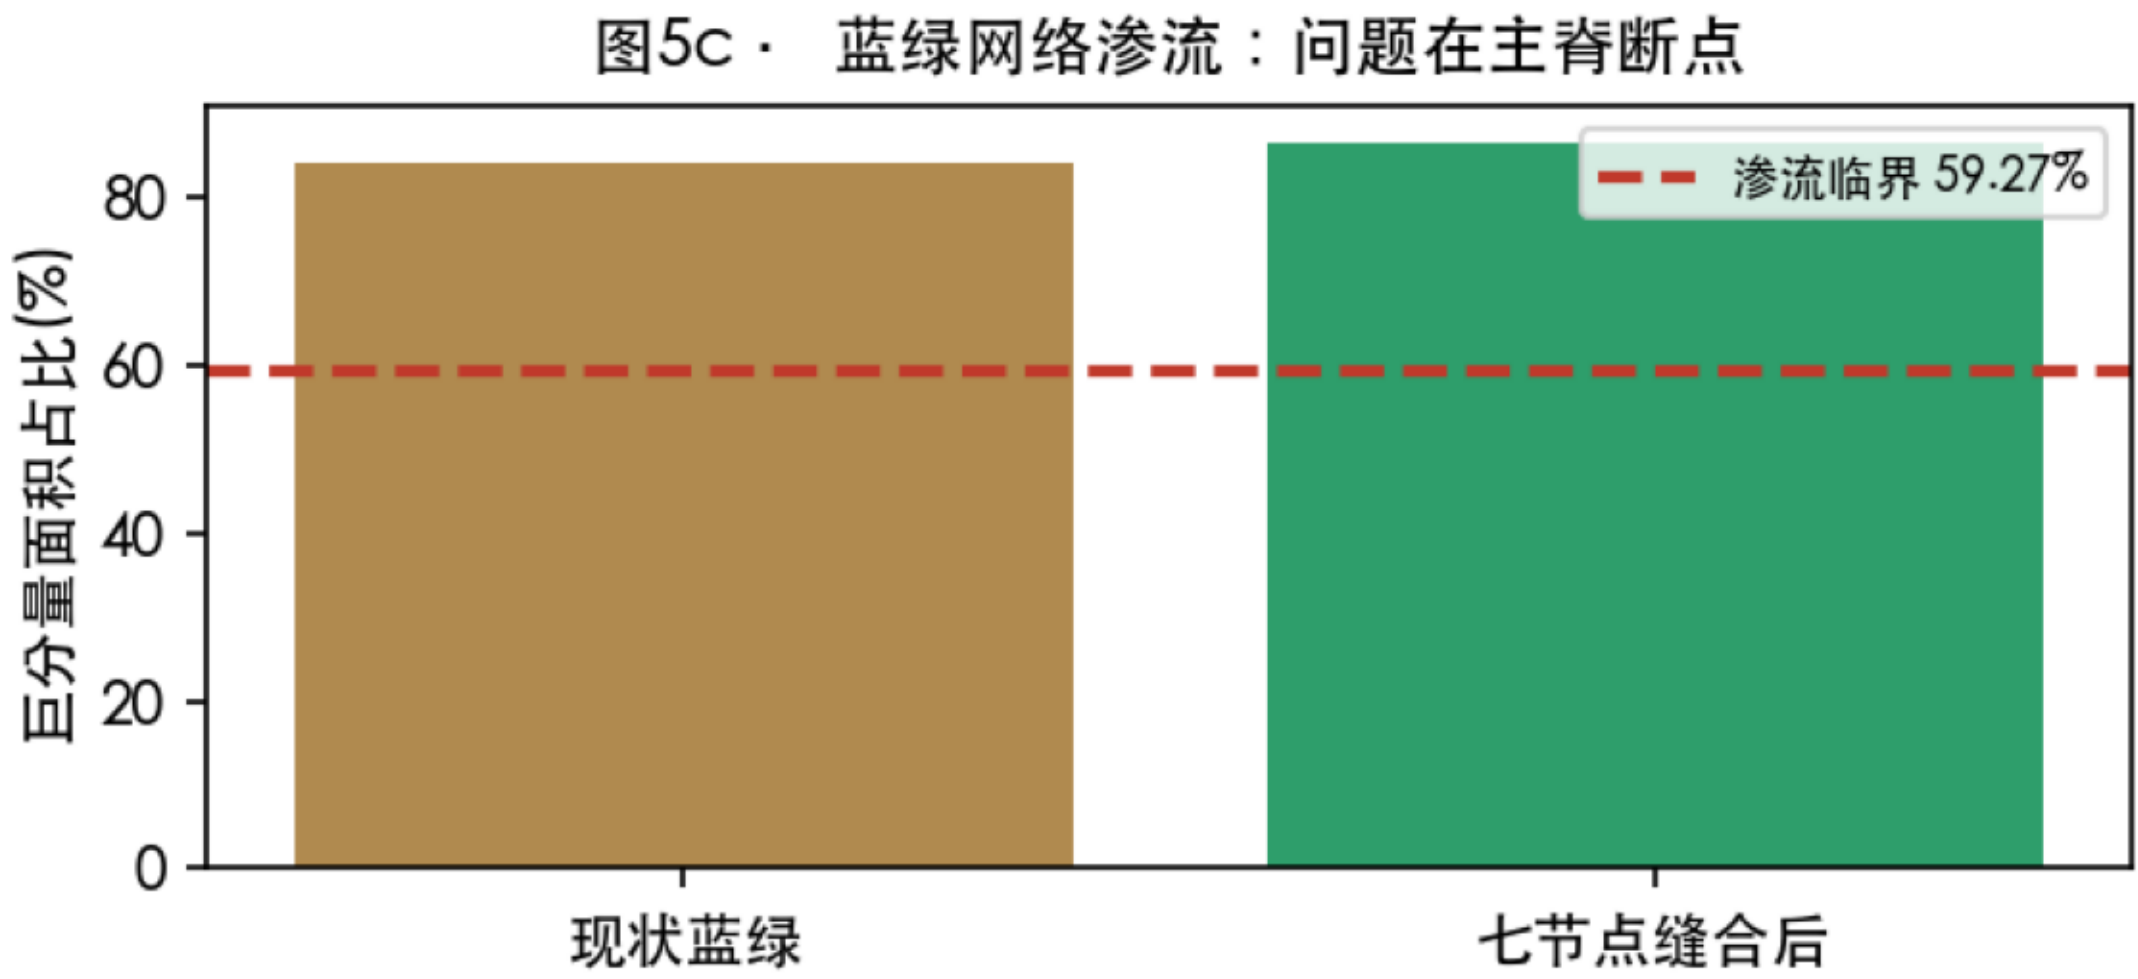

7处主干路断点→缝合步道(红线)；整合度提升：北京北+132% 大钟寺+102% 五道口+65%（空间句法实算）

图5 · 核心指标复算与证据链（数据源：7项本地实算 + 高德POI + OSM）

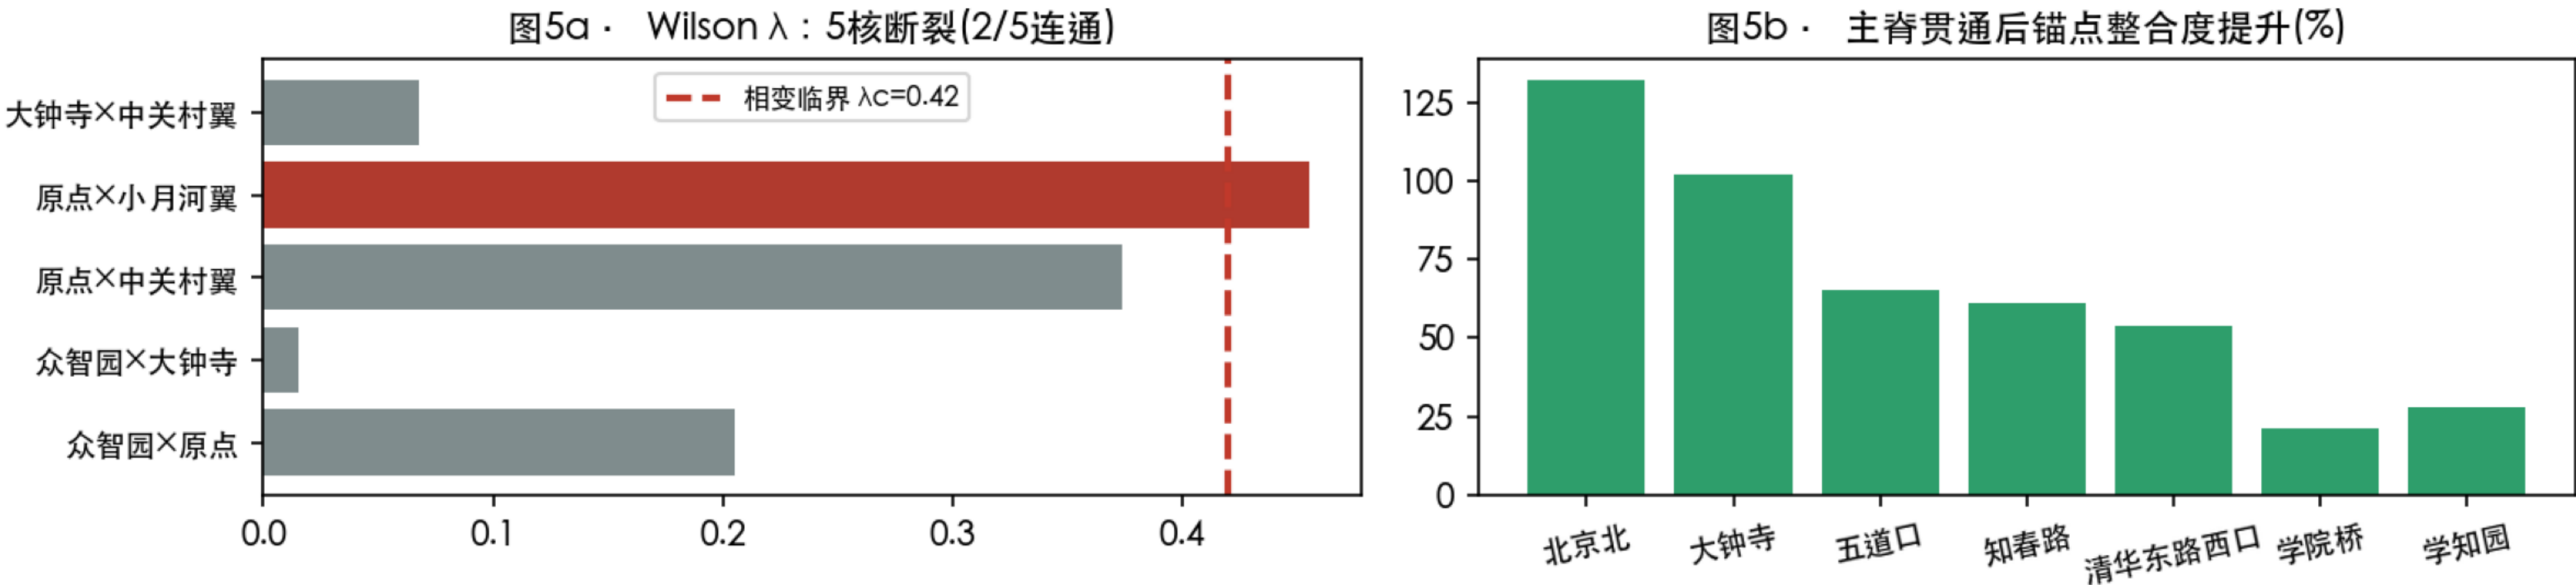

分形维 D(大尺度)

1.746

健康区间 1.6-1.8

POI 底座

25,476

12类 · 2026-08-15

交叉口密度

132.9/km²

老城>200 车本<80

绿地朝向熵

0.911

≈随机 >> 网格=0

图5d · 证据卡（全部可复算）



待确认

FAR/高度/红线

官方数据补齐后重算